



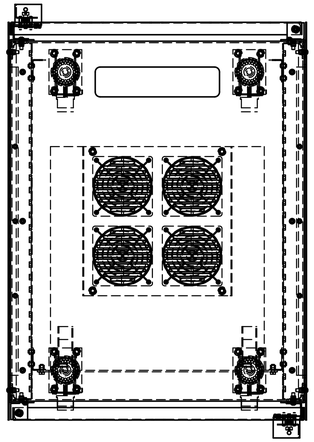


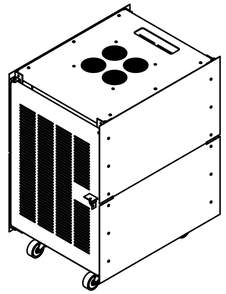

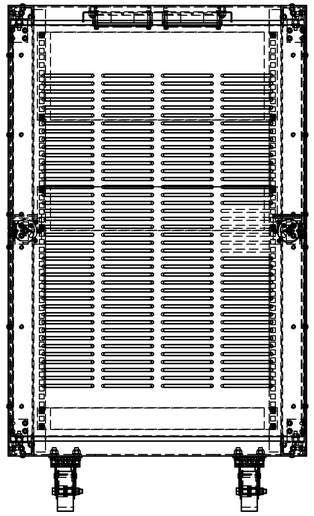

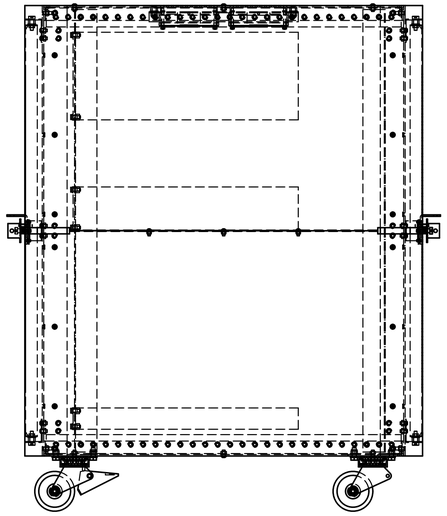

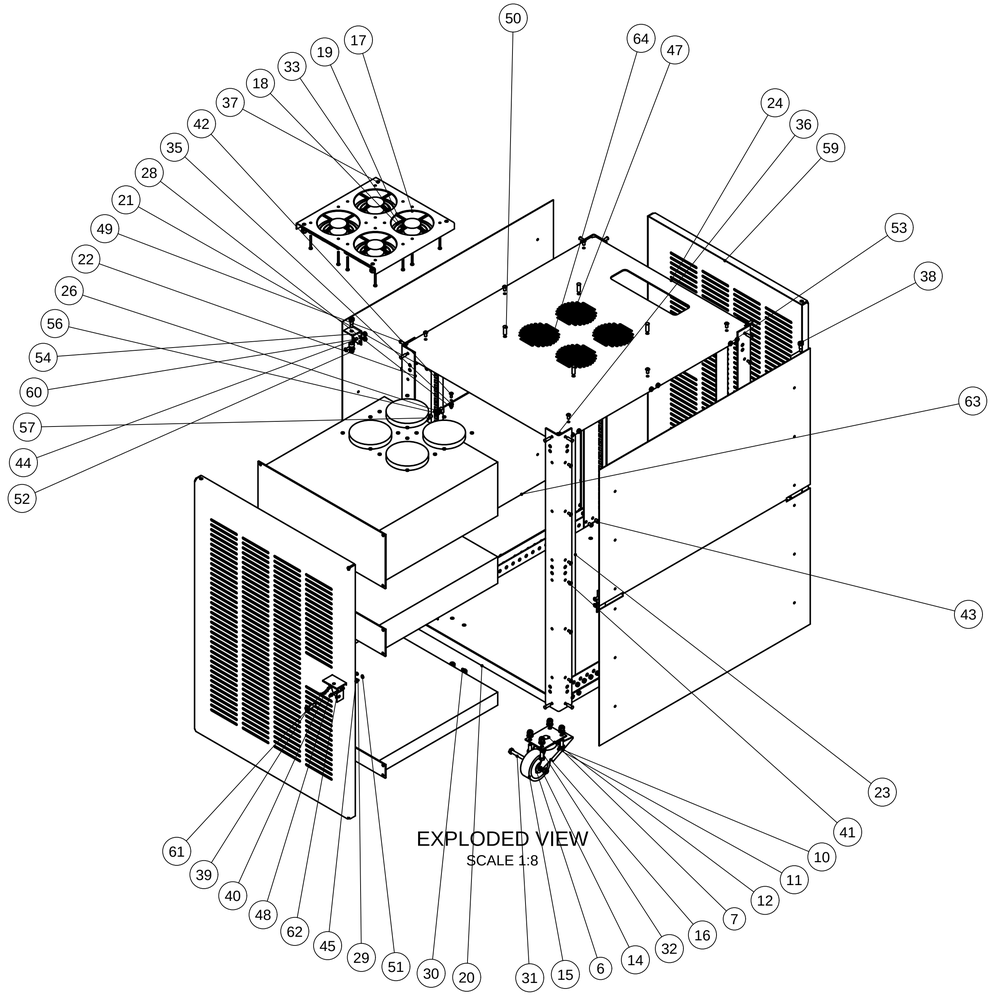


EXPLODED VIEW

SCALE 1:8

| ITEM | QTY | PART NUMBER | DESCRIPTION |
|---|---|---|---|
| 1 | 28 | ball_3969 | steel ball 3.969 (5/32"), ISO 3290 G100: the 608's balls |
| 2 | 176 | ball_4763 | steel ball 4.763 (3/16"), ISO 3290 G100: the caster's swivel ball rows |
| 3 | 4 | 608-2RS | inner ring: d 8, B 7, raceway groove |
| 4 | 4 | 608-2RS | outer ring: D 22, B 7, raceway groove, seal recesses |
| 5 | 8 | cage_half | 608 pressed steel ribbon cage, one half: flat web between 7 spherical |
| 6 | 4 | hub | caster wheel centre: nylon 6, hub 36 long (bosses 2.0 a side), bearing |
| 7 | 4 | kingpin | kingpin rivet 10.0: countersunk head flush in the plate, lower head 16 |
| 8 | 2 | lock_pin | caster lock pin 5.0 with a domed foot: the lever's cam lifts it into a race |
| 9 | 4 | lower_race | caster lower race: 2.5 steel washer, 36.0 ball track, 24 lock notches |
| 10 | 2 | pedal | caster total-lock pedal: 2.0 steel lever, pad, brake shoe and the lock pi |
| 11 | 2 | pedal_pin | caster pedal pivot pin 6.0, riveted heads 9.0 x 1.5 outside the yoke leg |
| 12 | 4 | plate | caster top plate 90 x 66 x 3.0 with the upper raceway and the kingpin' |
| 13 | 8 | 608-2RS | rubber seal 0.8 (one of two): in the outer ring's recess, lip on the inner |
| 14 | 8 | spacer | caster axle spacer: steel tube 8.2 ID x 12.0 OD x 14.70, leg to the bea |
| 15 | 4 | tread | caster tread: TPU 94 Sh A, 80 dia x 32 |
| 16 | 4 | yoke | caster yoke: pressed 2.5 swivel head with skirt and web, fork legs, axl |
| 17 | 4 | fan_120x25 | 120 x 120 x 25.4 axial fan, envelope (Delta AFB1212M-F00; any 120 |
| 18 | 4 | guard_120 | 120 mm wire finger guard (spec only, SPEC 7: holes on 105, loops 4. |
| 19 | 1 | RACK-401 | fan tray, t2 (SPEC 4, 5.9) |
| 20 | 1 | RACK-121 | base pan: 591 x 724 outer, t3, 30 flanges up (SPEC 5.2) |
| 21 | 4 | RACK-111 | rail carrier: L 32 (horizontal) x 40 (vertical) outer, t2, 714 long (SPEC 5 |
| 22 | 4 | RACK-101 | post: 50 x 50 L, t3, 906 long (SPEC 5.1) |
| 23 | 4 | RACK-201 | EIA rail: L 26.88 (mount face) x 45 (web) outer, t2, 890 long (SPEC 5. |
| 24 | 1 | RACK-131 | top pan: the base pan's outline, t3 (SPEC 5.2) |
| 25 | 4 | ball_4 | steel ball 4 (ISO 3290 G100) |
| 26 | 12 | cage_nut_m6 | M6 cage nut for 9.5 square holes (Rittal DK 2094.200), envelope |
| 27 | 6 | iso10511_m4 | ISO 10511 prevailing torque type hexagon thin nut with non-metallic i |
| 28 | 6 | iso10511_m5 | ISO 10511 prevailing torque type hexagon thin nut with non-metallic i |
| 29 | 18 | iso10511_m6 | ISO 10511 prevailing torque type hexagon thin nut with non-metallic i |
| 30 | 24 | iso10511_m8 | ISO 10511 prevailing torque type hexagon thin nut with non-metallic i |
| 31 | 4 | iso4014_m8x55 | ISO 4014 hexagon head bolt M8 x 55 |
| 32 | 16 | iso4017_m8x20 | ISO 4017 hexagon head screw M8 x 20 |
| 33 | 16 | iso7045_m4x40 | ISO 7045 cross recessed pan head screw M4 x 40 (fan screw) |
| 34 | 6 | iso7089_4 | ISO 7089 plain washer, size 4 |
| 35 | 6 | iso7089_5 | ISO 7089 plain washer, size 5 |
| 36 | 16 | iso7089_6 | ISO 7089 plain washer, size 6 |
| 37 | 24 | iso7089_8 | ISO 7089 plain washer, size 8 |
| 38 | 4 | iso7379_8x12_m6 | ISO 7379 hexagon socket shoulder screw 8 x 12, thread M6 x 11 |
| 39 | 2 | iso7379_8x16_m6 | ISO 7379 hexagon socket shoulder screw 8 x 16, thread M6 x 11 |
| 40 | 4 | iso7380_m4x25 | ISO 7380-1 hexagon socket button head screw M4 x 25 |
| 41 | 24 | iso7380_m5x10 | ISO 7380-1 hexagon socket button head screw M5 x 10 |
| 42 | 6 | iso7380_m5x12 | ISO 7380-1 hexagon socket button head screw M5 x 12 |
| 43 | 16 | iso7380_m6x10 | ISO 7380-1 hexagon socket button head screw M6 x 10 |
| 44 | 24 | iso7380_m6x12 | ISO 7380-1 hexagon socket button head screw M6 x 12 |
| 45 | 4 | latch_spacer_6x15 | steel round spacer 6.0 OD x 4.3 ID x 15.0 (latch link posts) |
| 46 | 2 | latch_spring_h8_17 | latch compression spring at height 8.17 (representative: wire 1.2, mea |
| 47 | 8 | nylon_spacer_8x14x8 | PA66 spacer 8.2 ID x 14 OD x 8.0 (hinge pins and fan tray hangers) |
| 48 | 6 | pem_fh_m4_12 | PEM FH-M4-12 flush-head self-clinching stud |
| 49 | 16 | pem_fh_m6_20 | PEM FH-M6-20 flush-head self-clinching stud |
| 50 | 4 | pem_fh_m8_25 | PEM FH-M8-25 flush-head self-clinching stud |
| 51 | 20 | pem_s_m4_0_t2 | PEM S-M4-0 self-clinching nut, as installed in a 1.88 sheet |
| 52 | 4 | pem_s_m6_0_t1 | PEM S-M6-0 self-clinching nut, as installed in a 1.52 sheet |
| 53 | 124 | pem_s_m6_0_t2 | PEM S-M6-0 self-clinching nut, as installed in a 1.88 sheet |
| 54 | 48 | pem_s_m6_0_t3 | PEM S-M6-0 self-clinching nut, as installed in a 3.02 sheet |
| 55 | 48 | pem_ss_m5_0_t3 | PEM SS-M5-0 self-clinching nut, as installed in a 3.02 sheet |
| 56 | 12 | plastic_washer_m6 | plastic washer for the M6 rack screw (supplied with Rittal DK 7094.11 |
| 57 | 12 | rack_screw_m6x16 | rack screw M6 x 16, slotted cheese head (Rittal DK 7094.110; head p |
| 58 | 2 | RACK-313 | latch cam, t2, flat (SPEC 5.8) |
| 59 | 2 | RACK-301 | door, t1 (SPEC 5.6, latch additions 5.8) |
| 60 | 4 | RACK-311 | hinge bracket, t2 (SPEC 5.7) |
| 61 | 2 | RACK-322 | latch base, t3 (SPEC 5.8) |
| 62 | 2 | RACK-321 | latch handle, t2 (SPEC 5.8) |
| 63 | 4 | RACK-141 | side half-panel, t1 (SPEC 5.5) |
| 64 | 2 | RACK-312 | strike, t2 (SPEC 5.8 rev, base as 5.8 rev A) |

| | | | |
|---|---|---|---|
| TITLE: RACK, 18U, GENERAL ASSEMBLY | | | COMPANY |
| DWG NO: RACK-001 | REV: A | SIZE: D | |
| MATERIAL | SCALE: 1:6 | SHEET: 1 OF 1 | |
| DRAWN: D. BASCOM | DATE | UNLESS NOTED | MASS |