



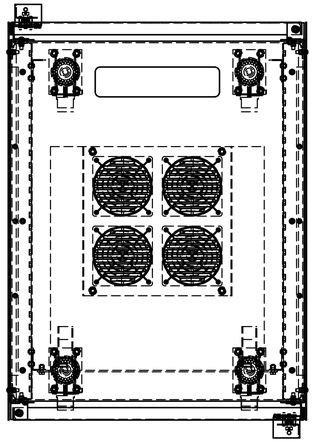


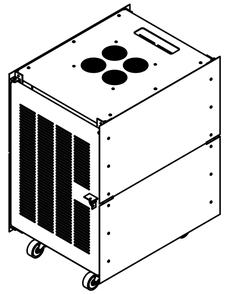

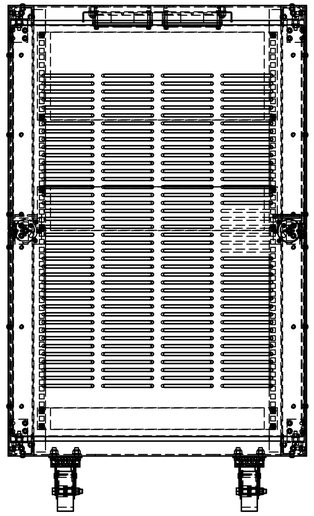

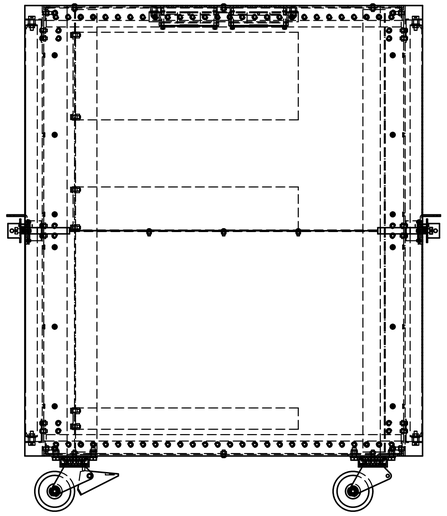


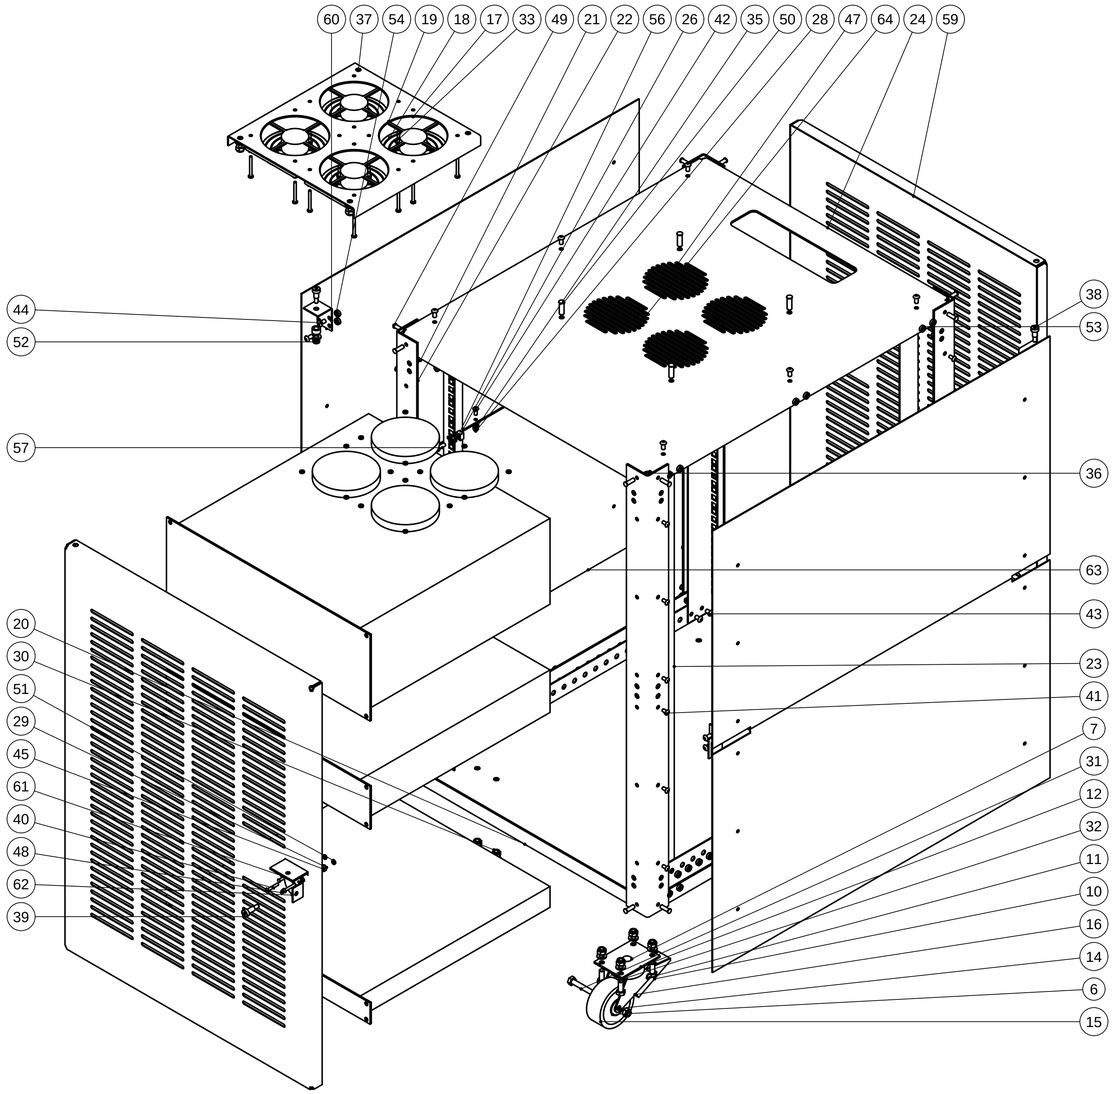


EXPLODED VIEW


SCALE 1:5


TITLE: RACK, 18U, GENERAL ASSEMBLY			COMPANY
DWG NO: RACK-001		REV: A	SIZE: D
MATERIAL		SCALE: 1:6	SHEET: 1 OF 2
DRAWN: D. BASCOM	DATE	UNLESS NOTED	MASS

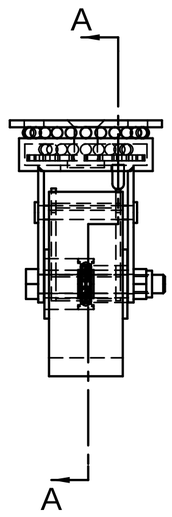

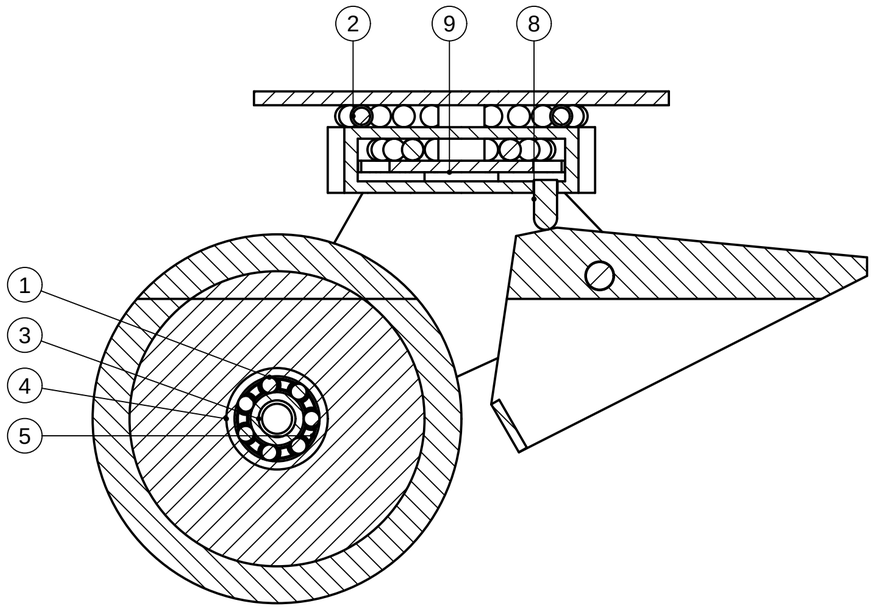

SECTION A-A
SCALE 1:1

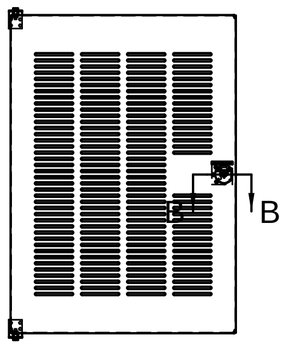

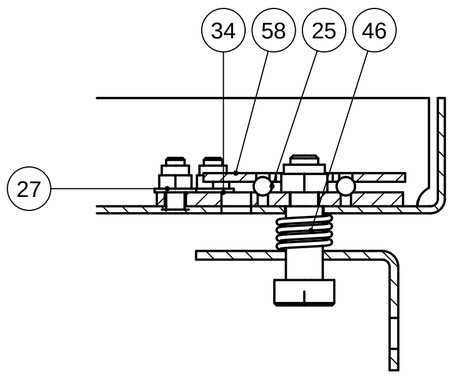

SECTION B-B
SCALE 1:1

ITEM	QTY	PART NUMBER	DESCRIPTION
60	4	RACK-311	hinge bracket, t2 (SPEC 5.7)
61	2	RACK-322	latch base, t3 (SPEC 5.8)
62	2	RACK-321	latch handle, t2 (SPEC 5.8)
63	4	RACK-141	side half-panel, t1 (SPEC 5.5)
64	2	RACK-312	strike, t2 (SPEC 5.8 rev, base as 5.8 rev A)

ITEM	QTY	PART NUMBER	DESCRIPTION
1	28	ball_3969	steel ball 3.969 (5/32"), ISO 3290 G100: the 608's balls
2	176	ball_4763	steel ball 4.763 (3/16"), ISO 3290 G100: the caster's swivel ball rows
3	4	608-2RS	inner ring: d 8, B 7, raceway groove
4	4	608-2RS	outer ring: D 22, B 7, raceway groove, seal recesses
5	8	cage_half	608 pressed steel ribbon cage, one half: flat web between 7 spherical pocket cups
6	4	hub	caster wheel centre: nylon 6, hub 36 long (bosses 2.0 a side), bearing bore 22 with a shoulder
7	4	kingpin	kingpin rivet 10.0: countersunk head flush in the plate, lower head 16 x 3 under the race
8	2	lock_pin	caster lock pin 5.0 with a domed foot: the lever's cam lifts it into a race notch
9	4	lower_race	caster lower race: 2.5 steel washer, 36.0 ball track, 24 lock notches
10	2	pedal	caster total-lock pedal: 2.0 steel lever, pad, brake shoe and the lock pin's cam edge
11	2	pedal_pin	caster pedal pivot pin 6.0, riveted heads 9.0 x 1.5 outside the yoke legs
12	4	plate	caster top plate 90 x 66 x 3.0 with the upper raceway and the kingpin's countersink
13	8	608-2RS	rubber seal 0.8 (one of two): in the outer ring's recess, lip on the inner ring's land
14	8	spacer	caster axle spacer: steel tube 8.2 ID x 12.0 OD x 14.70, leg to the bearing's inner ring
15	4	tread	caster tread: TPU 94 Sh A, 80 dia x 32
16	4	yoke	caster yoke: pressed 2.5 swivel head with skirt and web, fork legs, axle and pedal pin holes, loc
17	4	fan_120x25	120 x 120 x 25.4 axial fan, envelope (Delta AFB1212M-F00; any 120 x 25 frame with holes on 1
18	4	guard_120	120 mm wire finger guard (spec only, SPEC 7: holes on 105, loops 4.6, height ~5, ring wire 1.6,
19	1	RACK-401	fan tray, t2 (SPEC 4, 5.9)
20	1	RACK-121	base pan: 591 x 724 outer, t3, 30 flanges up (SPEC 5.2)
21	4	RACK-111	rail carrier: L 32 (horizontal) x 40 (vertical) outer, t2, 714 long (SPEC 5.3, rev B R7)
22	4	RACK-101	post: 50 x 50 L, t3, 906 long (SPEC 5.1)
23	4	RACK-201	EIA rail: L 26.88 (mount face) x 45 (web) outer, t2, 890 long (SPEC 5.4)
24	1	RACK-131	top pan: the base pan's outline, t3 (SPEC 5.2)
25	4	ball_4	steel ball 4 (ISO 3290 G100)
26	12	cage_nut_m6	M6 cage nut for 9.5 square holes (Rittal DK 2094.200), envelope
27	6	iso10511_m4	ISO 10511 prevailing torque type hexagon thin nut with non-metallic insert M4
28	6	iso10511_m5	ISO 10511 prevailing torque type hexagon thin nut with non-metallic insert M5
29	18	iso10511_m6	ISO 10511 prevailing torque type hexagon thin nut with non-metallic insert M6
30	24	iso10511_m8	ISO 10511 prevailing torque type hexagon thin nut with non-metallic insert M8
31	4	iso4014_m8x55	ISO 4014 hexagon head bolt M8 x 55
32	16	iso4017_m8x20	ISO 4017 hexagon head screw M8 x 20
33	16	iso7045_m4x40	ISO 7045 cross recessed pan head screw M4 x 40 (fan screw)
34	6	iso7089_4	ISO 7089 plain washer, size 4
35	6	iso7089_5	ISO 7089 plain washer, size 5
36	16	iso7089_6	ISO 7089 plain washer, size 6
37	24	iso7089_8	ISO 7089 plain washer, size 8
38	4	iso7379_8x12_m6	ISO 7379 hexagon socket shoulder screw 8 x 12, thread M6 x 11
39	2	iso7379_8x16_m6	ISO 7379 hexagon socket shoulder screw 8 x 16, thread M6 x 11
40	4	iso7380_m4x25	ISO 7380-1 hexagon socket button head screw M4 x 25
41	24	iso7380_m5x10	ISO 7380-1 hexagon socket button head screw M5 x 10
42	6	iso7380_m5x12	ISO 7380-1 hexagon socket button head screw M5 x 12
43	16	iso7380_m6x10	ISO 7380-1 hexagon socket button head screw M6 x 10
44	24	iso7380_m6x12	ISO 7380-1 hexagon socket button head screw M6 x 12
45	4	latch_spacer_6x15	steel round spacer 6.0 OD x 4.3 ID x 15.0 (latch link posts)
46	2	latch_spring_h8_17	latch compression spring at height 8.17 (representative: wire 1.2, mean diameter 10.8, 4 turns)
47	8	nylon_spacer_8x14x8	PA66 spacer 8.2 ID x 14 OD x 8.0 (hinge pins and fan tray hangers)
48	6	pem_fh_m4_12	PEM FH-M4-12 flush-head self-clinching stud
49	16	pem_fh_m6_20	PEM FH-M6-20 flush-head self-clinching stud
50	4	pem_fh_m8_25	PEM FH-M8-25 flush-head self-clinching stud
51	20	pem_s_m4_0_t2	PEM S-M4-0 self-clinching nut, as installed in a 1.88 sheet
52	4	pem_s_m6_0_t1	PEM S-M6-0 self-clinching nut, as installed in a 1.52 sheet
53	124	pem_s_m6_0_t2	PEM S-M6-0 self-clinching nut, as installed in a 1.88 sheet
54	48	pem_s_m6_0_t3	PEM S-M6-0 self-clinching nut, as installed in a 3.02 sheet
55	48	pem_ss_m5_0_t3	PEM SS-M5-0 self-clinching nut, as installed in a 3.02 sheet
56	12	plastic_washer_m6	plastic washer for the M6 rack screw (supplied with Rittal DK 7094.110)
57	12	rack_screw_m6x16	rack screw M6 x 16, slotted cheese head (Rittal DK 7094.110; head per ISO 1207)
58	2	RACK-313	latch cam, t2, flat (SPEC 5.8)
59	2	RACK-301	door, t1 (SPEC 5.6, latch additions 5.8)

TITLE: RACK, 18U, PARTS LIST			COMPANY:
DWG NO: RACK-001	REV: A		SIZE: C
MATERIAL:	SCALE: 1:2		SHEET: 2 OF 2
DRAWN: D. BASCOM	DATE:	UNLESS NOTED:	MASS: